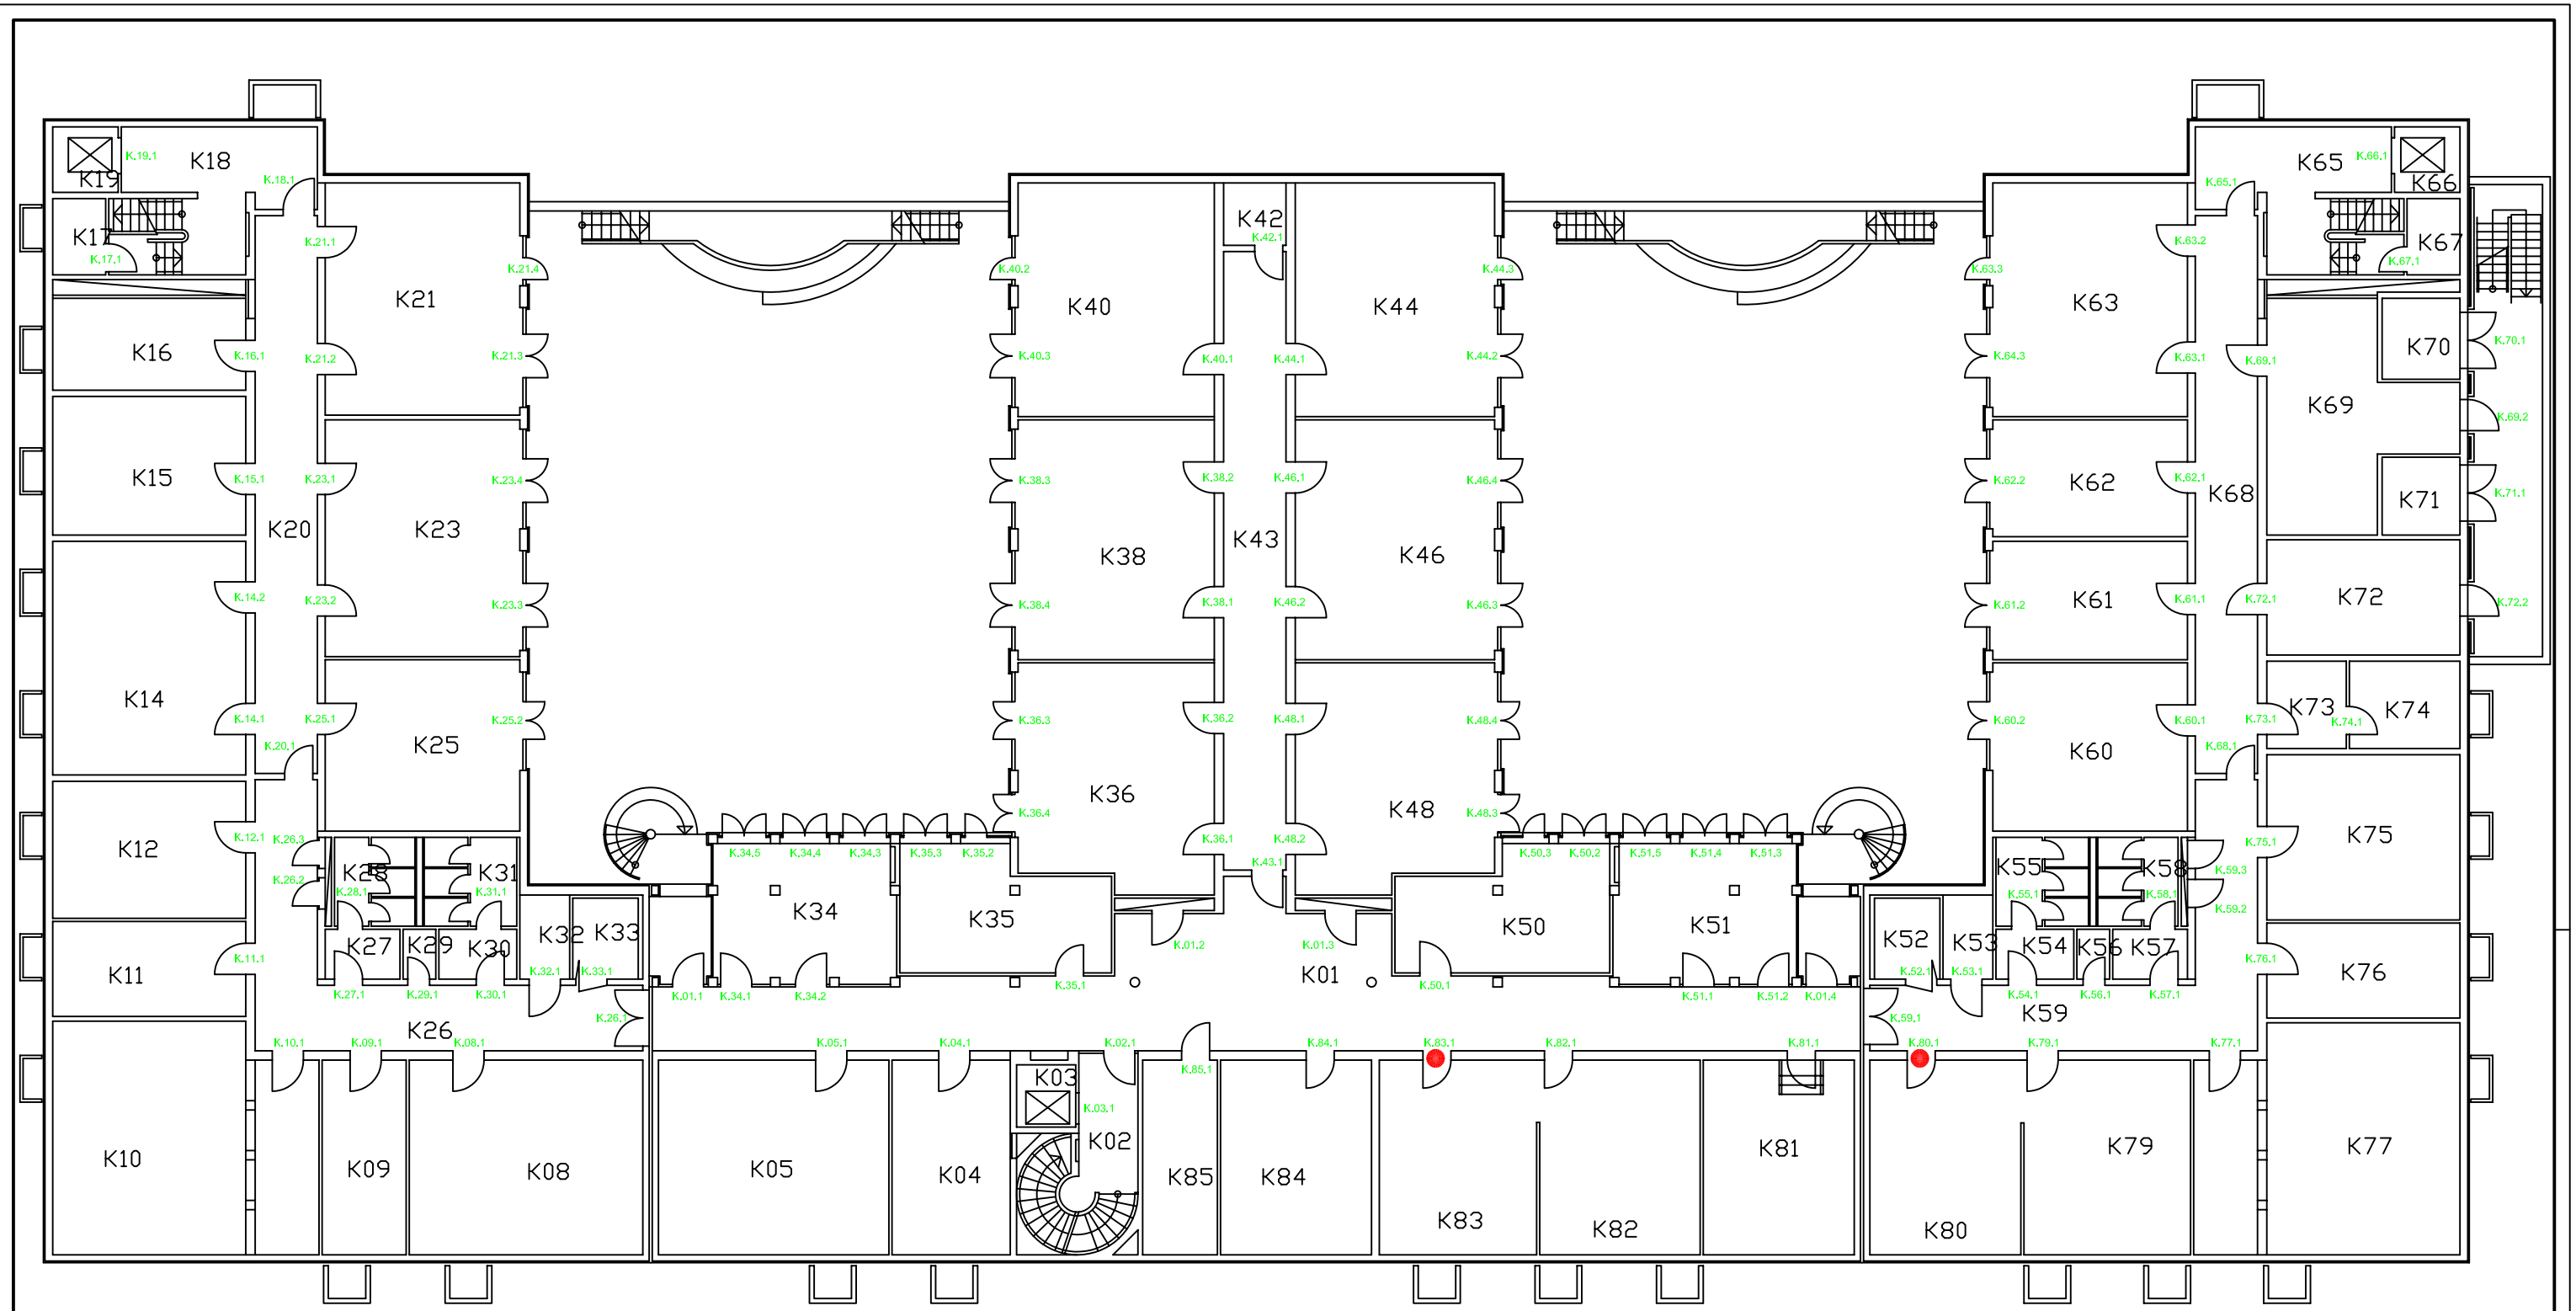

Onlinetür

Unterschrift Genius:		Planstand: Ausführungsplanung	Alle Maße sind am Bau zu prüfen !

Index	Datum	Änderung	Bearbeiter	CAD

GENIUS Ingenieurbüro GmbH

Treskowallee 30, 10318 Berlin
Tel.: 030 / 81 85 84 0
Fax : 030 / 81 85 84 99
mail: info@itgenius.de
www.itgenius.de

BAUVORHABEN: Freie Universität Berlin
Takustrasse 9
Zutrittskontrolle

PLAN: Kellergeschoss
Installationsplan

PROJEKT-NR.: 05-17

Datum:	10.06.2008
Bearbeiter:	Vo
CAD:	Vo
Maßstab:	1:100
Zeichnungs-Nr.:	05-17.A/Z-IP 9KG